Cuadro de Mando
y Proteccion
PLANTA +27.52. CB1

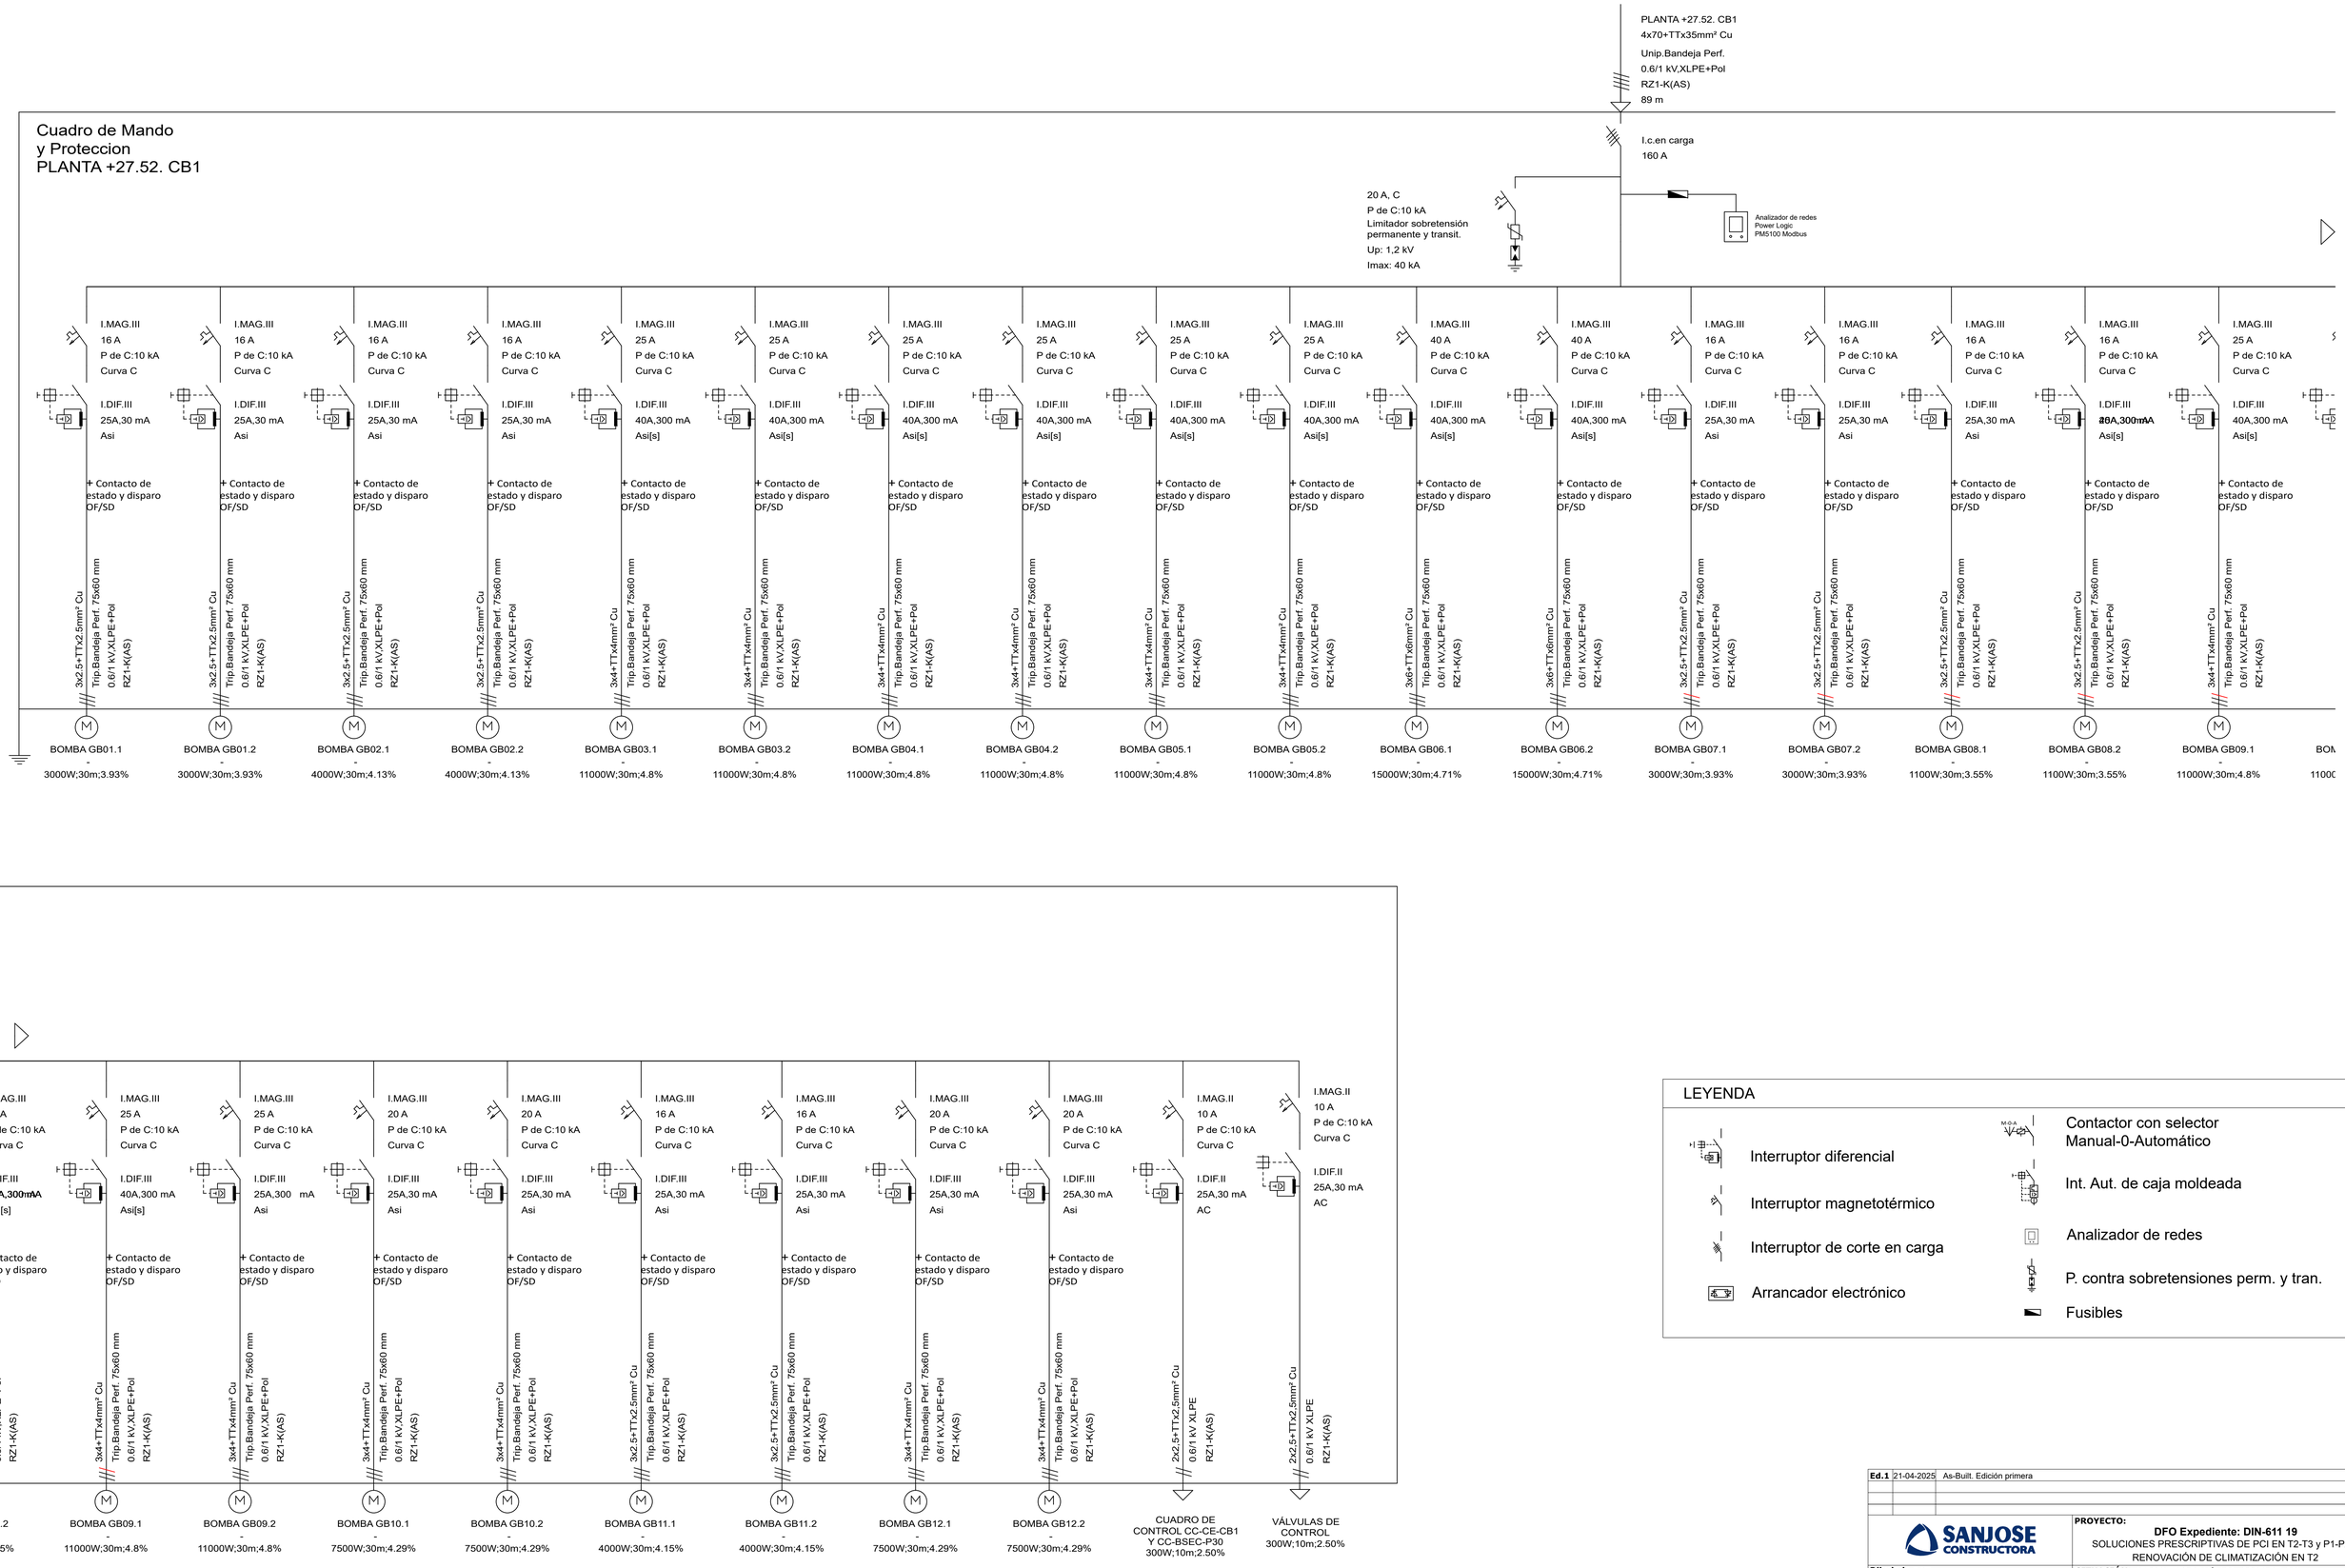

LEYENDA

- Interruptor diferencial
- Interruptor magnetotérmico
- Interruptor de corte en carga
- Arrancador electrónico
- Contactor con selector Manual-0-Automático
- Int. Aut. de caja moldeada
- Analizador de redes
- P. contra sobretensiones perm. y tran.
- Fusibles

Ed.1	21-04-2025	As-Built. Edición primera

SANJOSE CONSTRUCTORA

PROYECTO: **DFO Expediente: DIN-611 19**
SOLUCIONES PRESCRIPTIVAS DE PCI EN T2-T3 y P1-P2 Y RENOVACIÓN DE CLIMATIZACIÓN EN T2

SITUACIÓN: AEROPUERTO DE MÁLAGA - COSTA DEL SOL

Dibujado por: EUGENIO A. DEL CID GARRIDO
Comprobado por: EUGENIO A. DEL CID GARRIDO
Aprobado por: EUGENIO A. DEL CID GARRIDO
ARCHIVO: 050307 Electricidad. Esquemas unifilares

PLANO: ELECTRICIDAD. ESQUEMAS UNIFILARES
CUADRO C6
(BOMBEO PRIMARIO)

N. PLANO: 050307
N. HOJA: 12/17
ESCALA: A1: S/E A3: S/E